
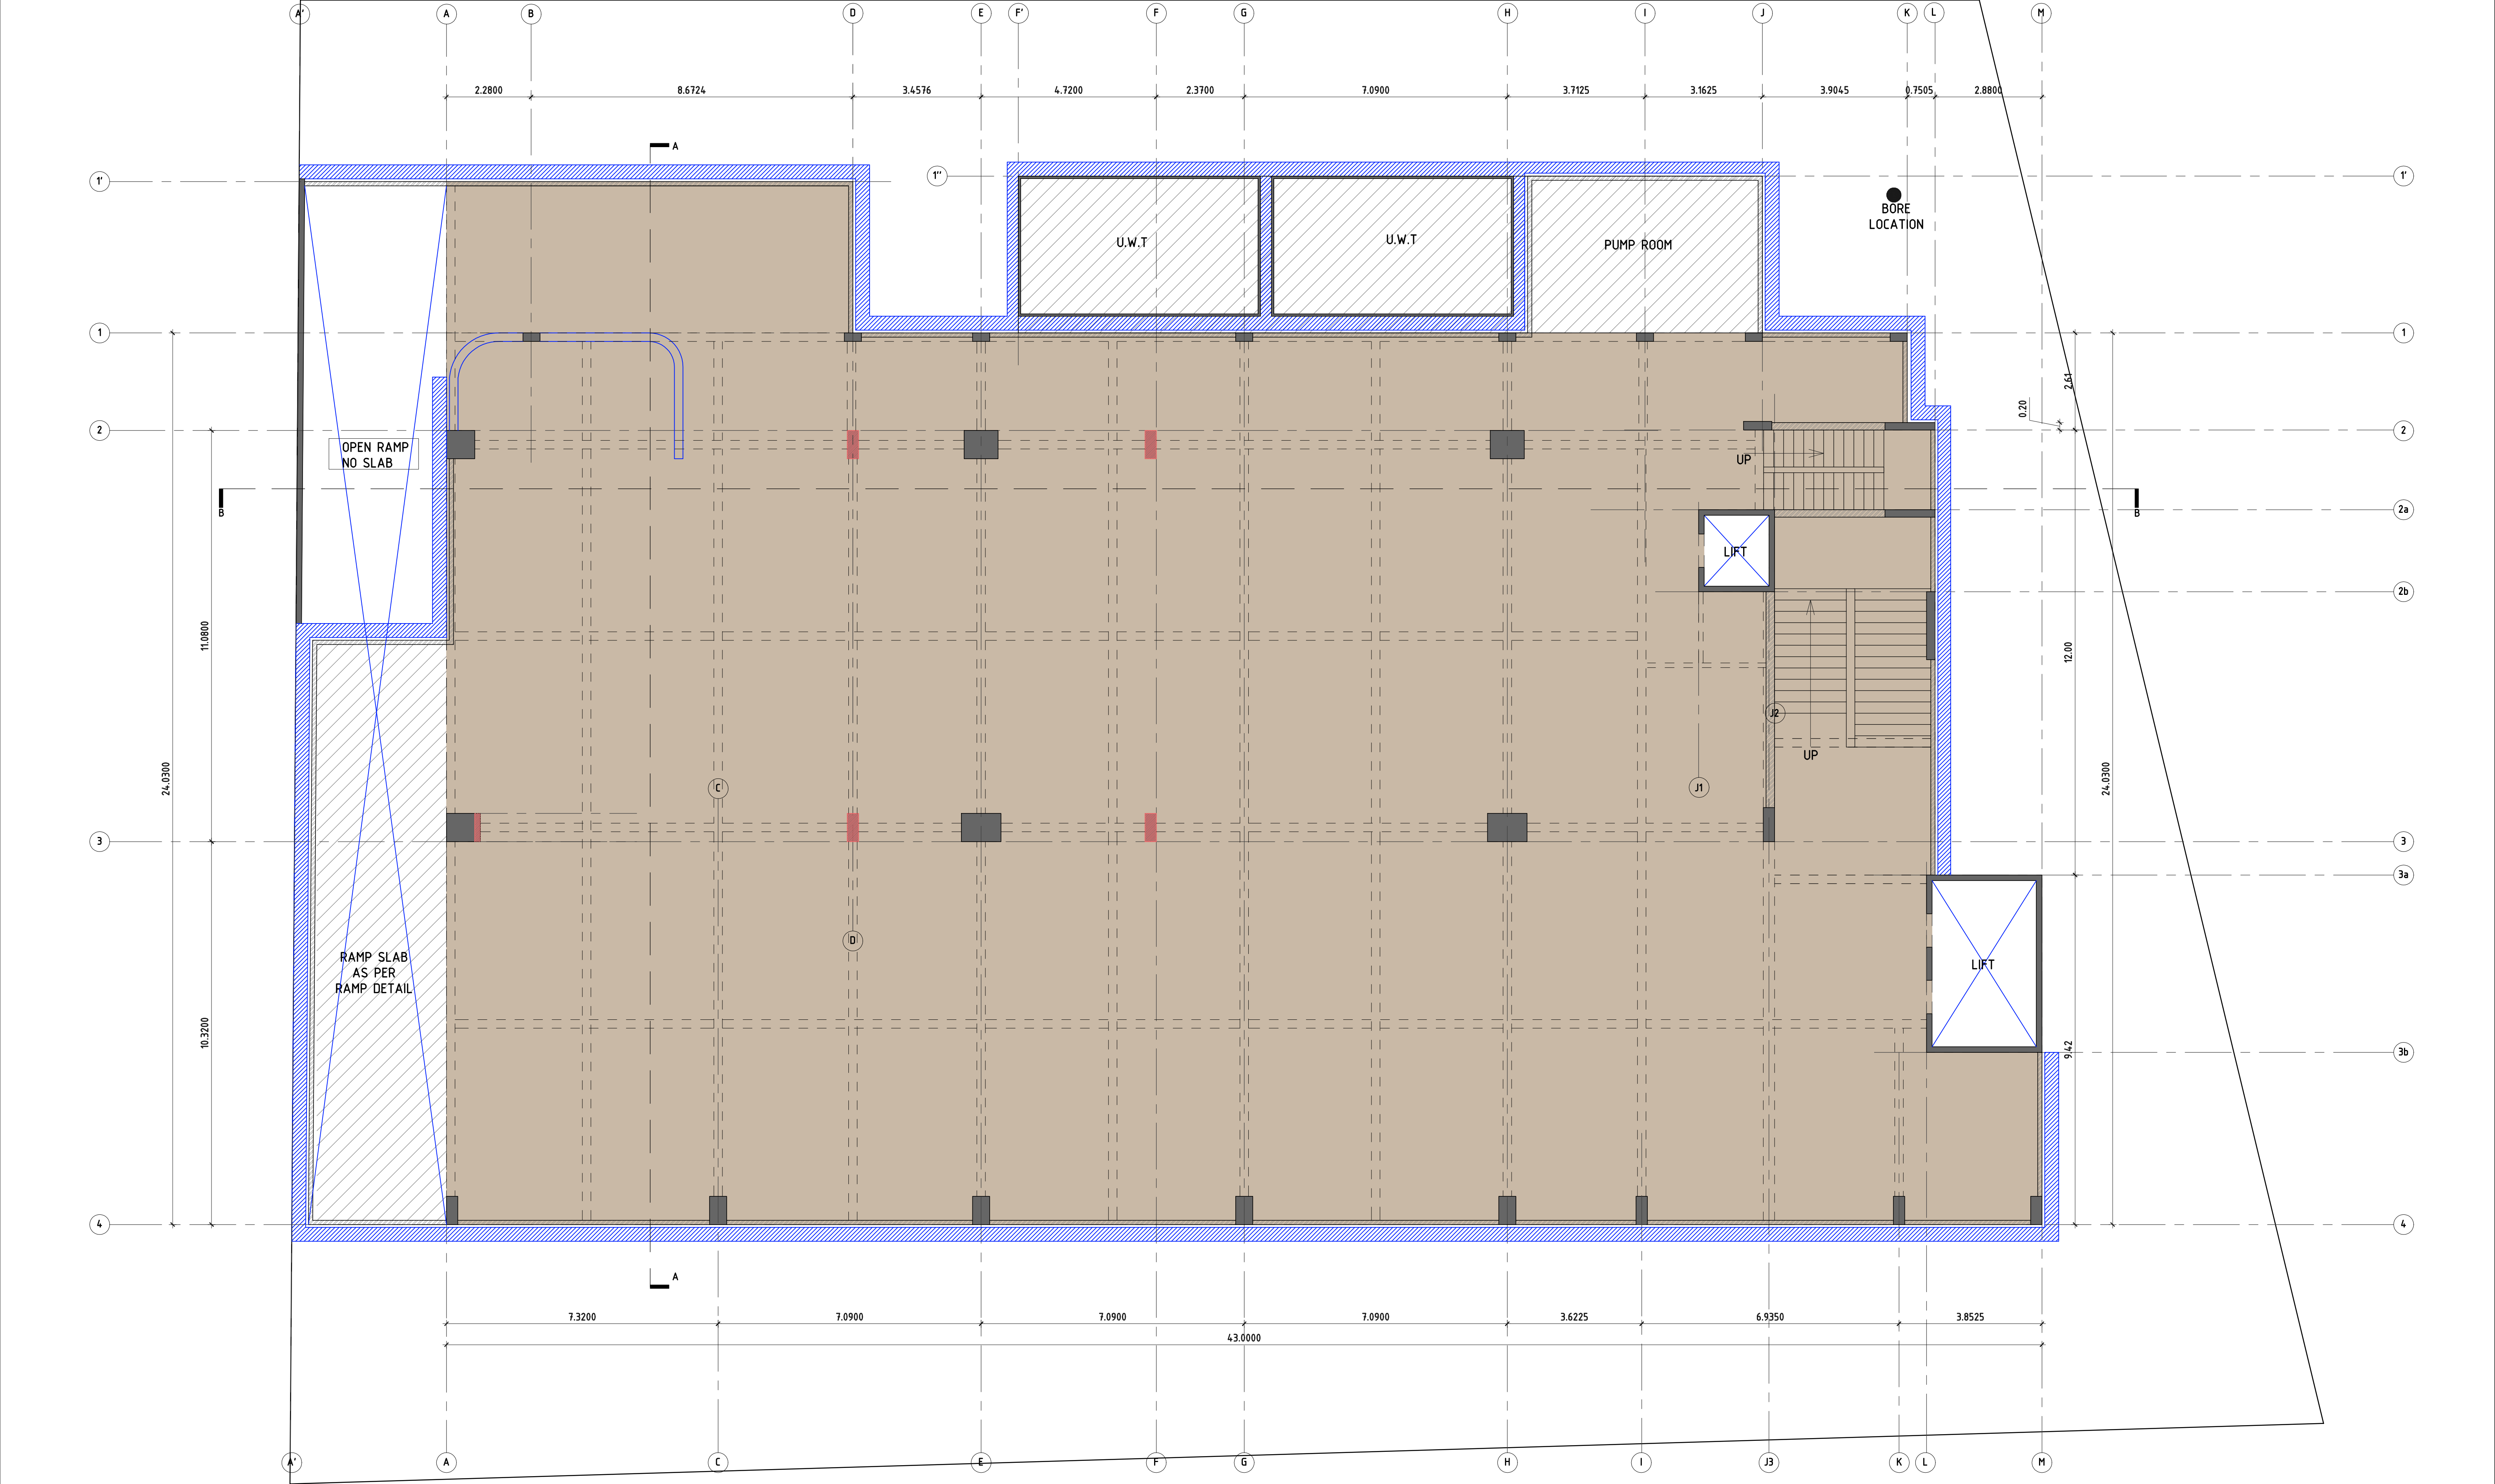


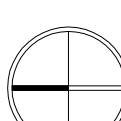


GENERAL NOTES :

- ALL DIMENSIONS ARE IN METRE
- ALL MEASUREMENTS ARE FROM UNFINISHED SURFACE TO UNFINISHED SURFACE. UNTILL OTHER SPECIFIED
- ALL DIMENSIONS ARE TO BE READ AND NOT TO BE MEASURED.
- DRIP MOULD IS TO BE PROVIDED AT ALL EXTERNAL WINDOW LINTELS
- CHICKEN MESH TO BE PROVIDED AT EVERY JUNCTION OF BRICK AND CONCRETE TO BE PLASTERED.
- IN CASE OF ANY AMBIGUITIES ON SITE, TH ARCHITECT SHOULD BE INFORMED.
- IT IS MUST TO INFORM AND TO HAVE PRIOR PERMISSION OF ARCHITECT BEFORE MAKING ANY CHANGES ON SITE.
- REFER THE LATEST REVISED DRAWING.
- IT IS MUST FOR RESPECTIVE SITE ENGINEER TO CHECK & CO-RELATE STRUCTURAL DRAWINGS WITH ARCHITECTURAL DRAWINGS


- ALL RCC WORKS, FOUNDATION & U.G.W.T DETAILS TO BE APPROVED FROM STRUCTURAL ENGINEER.
- ALL DRAWINGS SHALL BE READ IN CONJUNCTION WITH ALL OTHER RELEVANT DRAWINGS, TOGETHER WITH THE SPECIFICATIONS.
- IN CASE OF ANY DISCREPANCY BETWEEN ARCHITECTURAL DRGS. AND OTHER DRGS, DISCREPANCY SHOULD BE BROUGHT TO THE NOTICE OF THE ARCHITECT BEFORE COMMENCEMENT OF THE WORK.

DRAWING DETAIL				CLIENT	CONSULTANTS
BASEMENT LAYOUT PLAN ONLY FOR REFERENCE					
DWG NO	DATE		NORTH	ROYAL LANDMARK HOTEL	STRUCTURE : Modi consultant - 91-9904752590
PL-201	R0	05 DEC 2025			
	R1				
	R2				
DWG BY	CHECKED		SCALE		
NIRALEE	BIPINCHANDRA		N.T.S		

PROJECT	ROYAL LANDMARK HOTEL AT HIMMATNAGAR
	अवसिति AVASITI DESGIN CONSULTANCY PVT. LTD. 401,SHASTRA, OPP.DRIVE IN CINEMA, DRIVE IN ROAD, AHMEDABAD -380054,GUJARAT,INDIA E : adc@avasiti.in , www.avasiti.in PH: 079 40323308

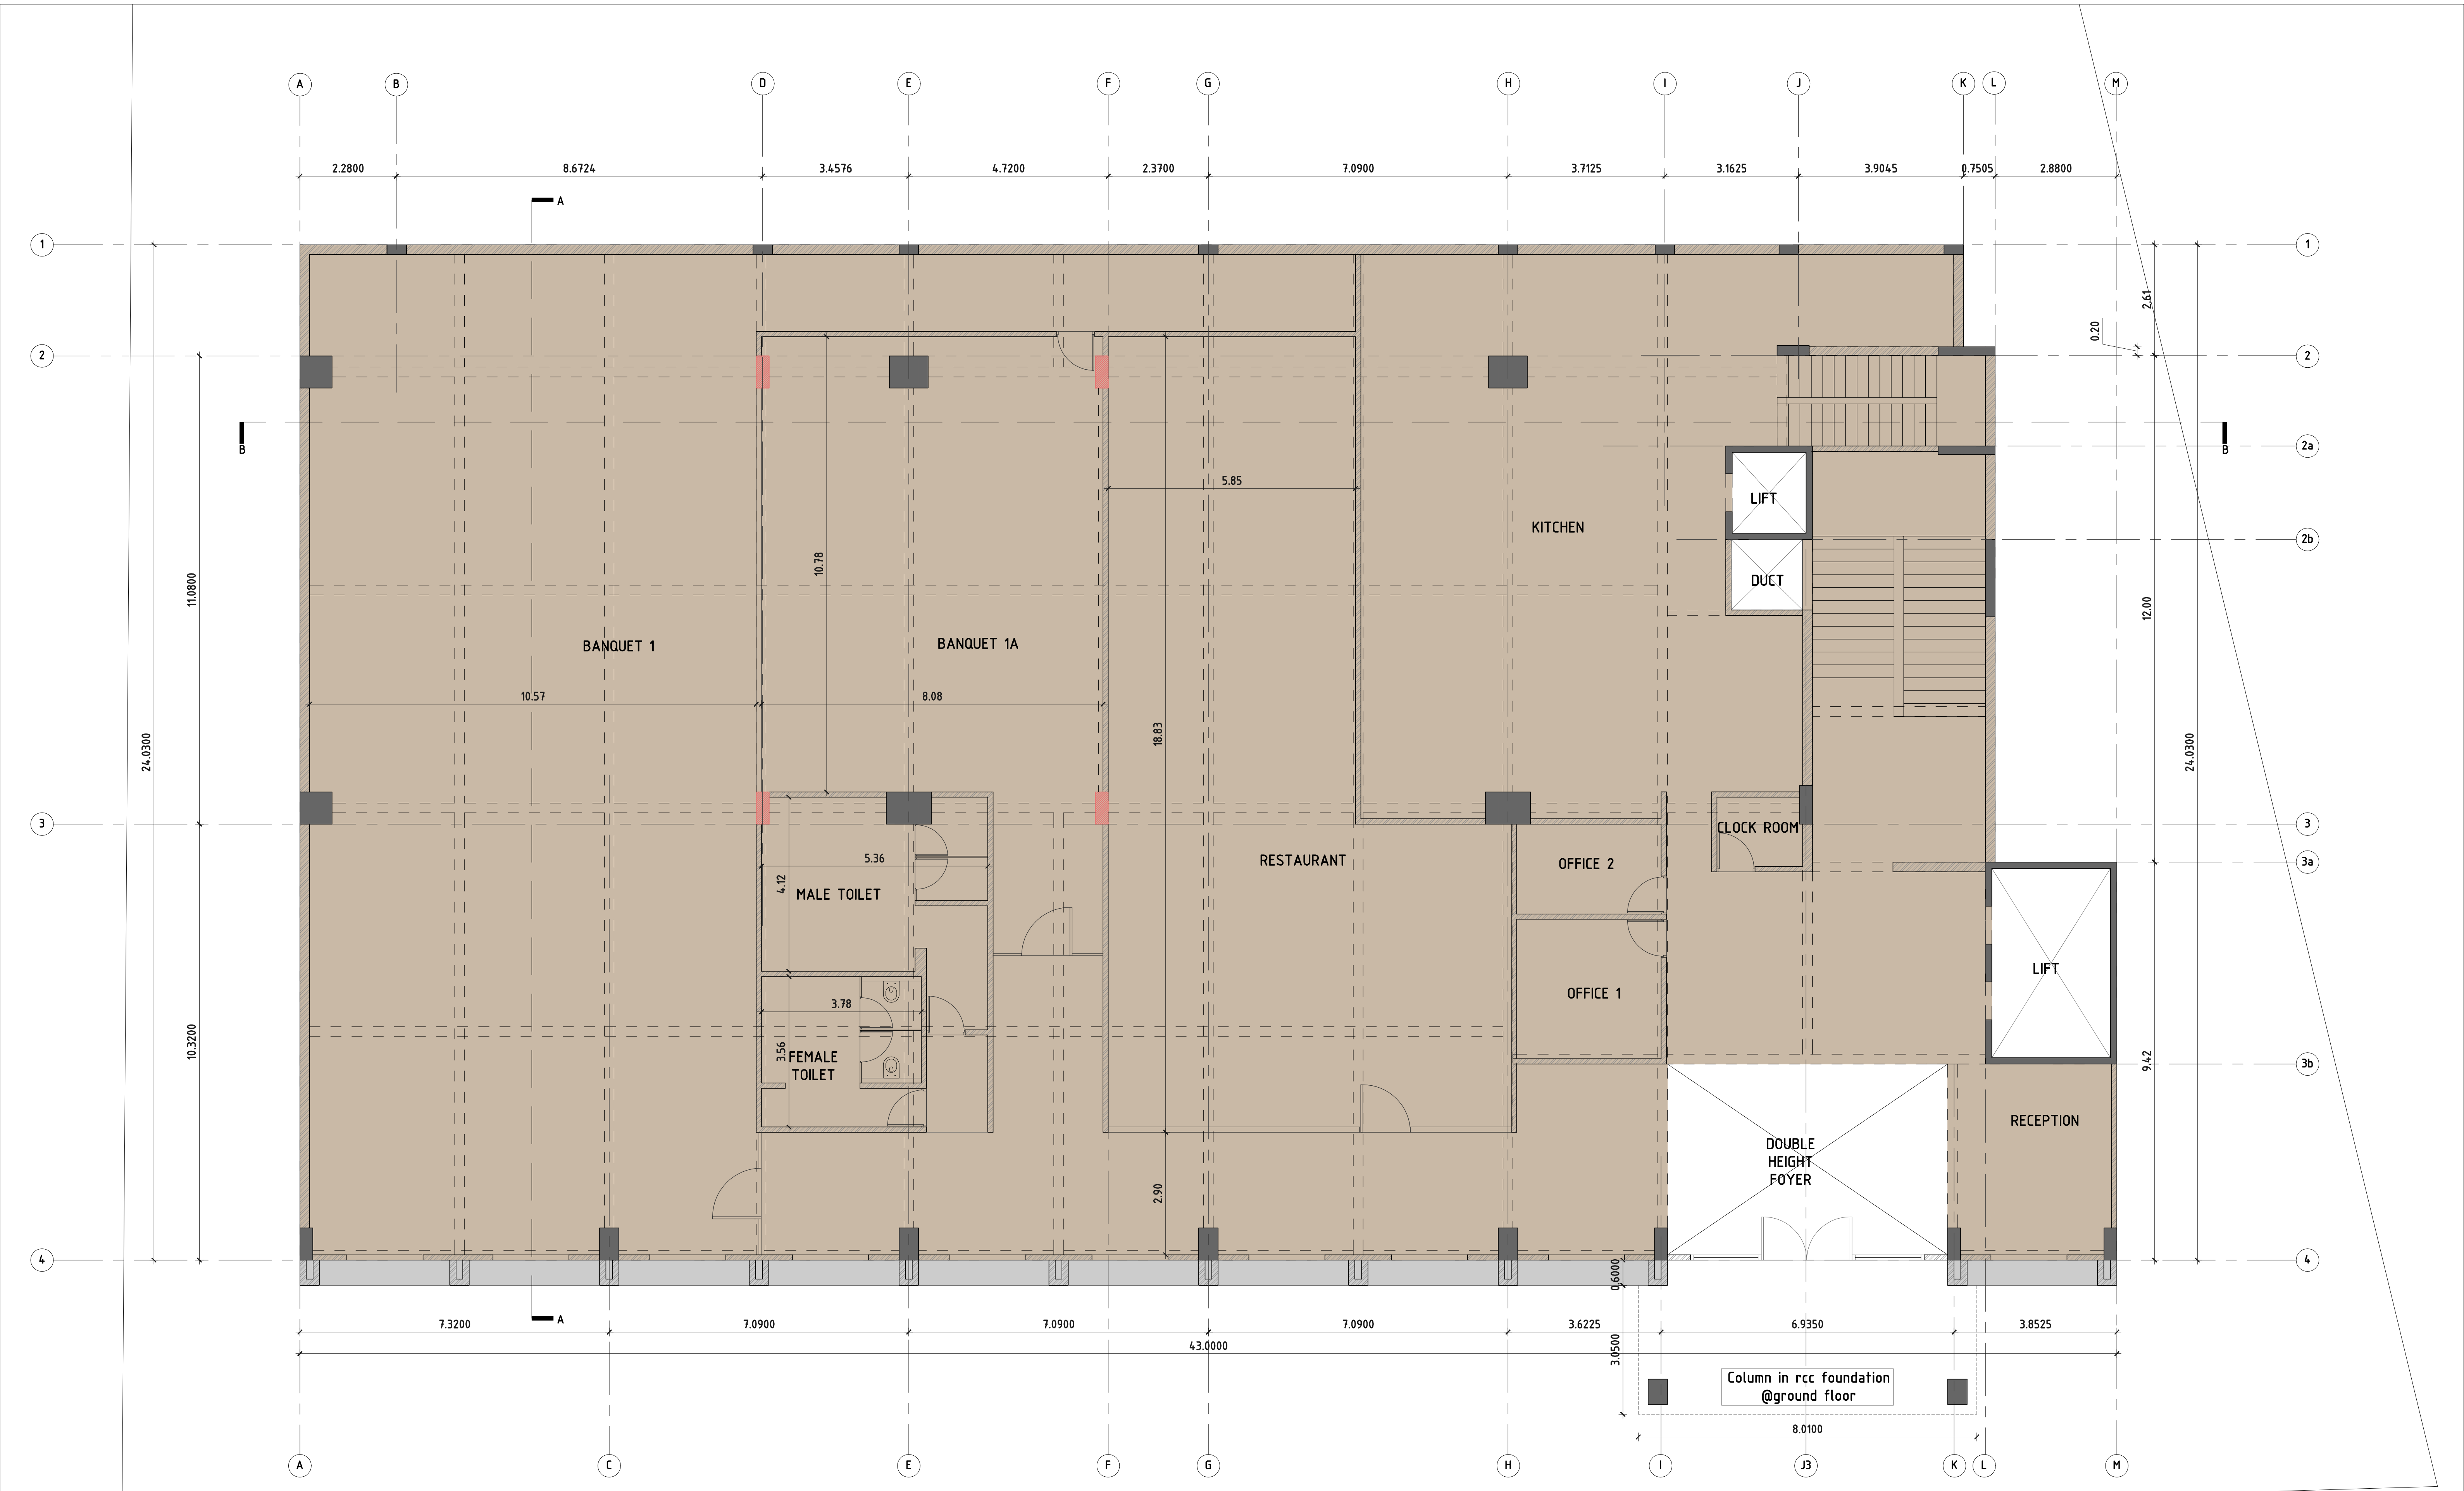

GENERAL NOTES :	● ALL DIMENSIONS ARE IN METRE ● ALL MEASUREMENTS ARE FROM UNFINISHED SURFACE TO UNFINISHED SURFACE. UNTILL OTHER SPECIFIED ● ALL DIMENSIONS ARE TO BE READ AND NOT TO BE MEASURED. ● DRIP MOULD IS TO BE PROVIDED AT ALL EXTERNAL WINDOW LINTELS ● CHICKEN MESH TO BE PROVIDED AT EVERY JUNCTION OF BRICK AND CONCRETE TO BE PLASTERED. ● IN CASE OF ANY AMBIGUITIES ON SITE, TH ARCHITECT SHOULD BE INFORMED. ● IT IS MUST TO INFORM AND TO HAVE PRIOR PERMISSION OF ARCHITECT BEFORE MAKING ANY CHANGES ON SITE. ● REFER THE LATEST REVISED DRAWING. ● IT IS MUST FOR RESPECTIVE SITE ENGINEER TO CHECK & CO-RELATE STRUCTURAL DRAWINGS WITH ARCHITECTURAL DRAWINGS			● ALL RCC WORKS, FOUNDATION & U.G.W.T DETAILS TO BE APPROVED FROM STRUCTURAL ENGINEER. ● ALL DRAWINGS SHALL BE READ IN CONJUNCTION WITH ALL OTHER RELEVANT DRAWINGS, TOGETHER WITH THE SPECIFICATIONS. ● IN CASE OF ANY DISCREPANCY BETWEEN ARCHITECTURAL DRGS. AND OTHER DRGS, DISCREPANCY SHOULD BE BROUGHT TO THE NOTICE OF THE ARCHITECT BEFORE COMMENCEMENT OF THE WORK.			
	DRAWING DETAIL	GROUND LAYOUT PLAN ONLY FOR REFERENCE			CLIENT	ROYAL LANDMARK HOTEL	
		DWG NO	DATE		NORTH	CONSULTANTS	STRUCTURE : Modi consultant - 91-9904752590
		PL-202	R0	05 DEC 2025			
			R1				
			R2				
	DWG BY	CHECKED	SCALE				
	NIRALEE	BIPINCHANDRA	N.T.S				
PROJECT			25001	ROYAL LANDMARK HOTEL AT HIMMATNAGAR			
ARCHITECT			अवसिति AVASITI DESGIN CONSULTANCY PVT. LTD. 401,SHASTRA, OPP.DRIVE IN CINEMA, DRIVE IN ROAD, AHMEDABAD -380054,GUJARAT,INDIA E : adc@avasiti.in , www.avasiti.in PH: 079 40323308				

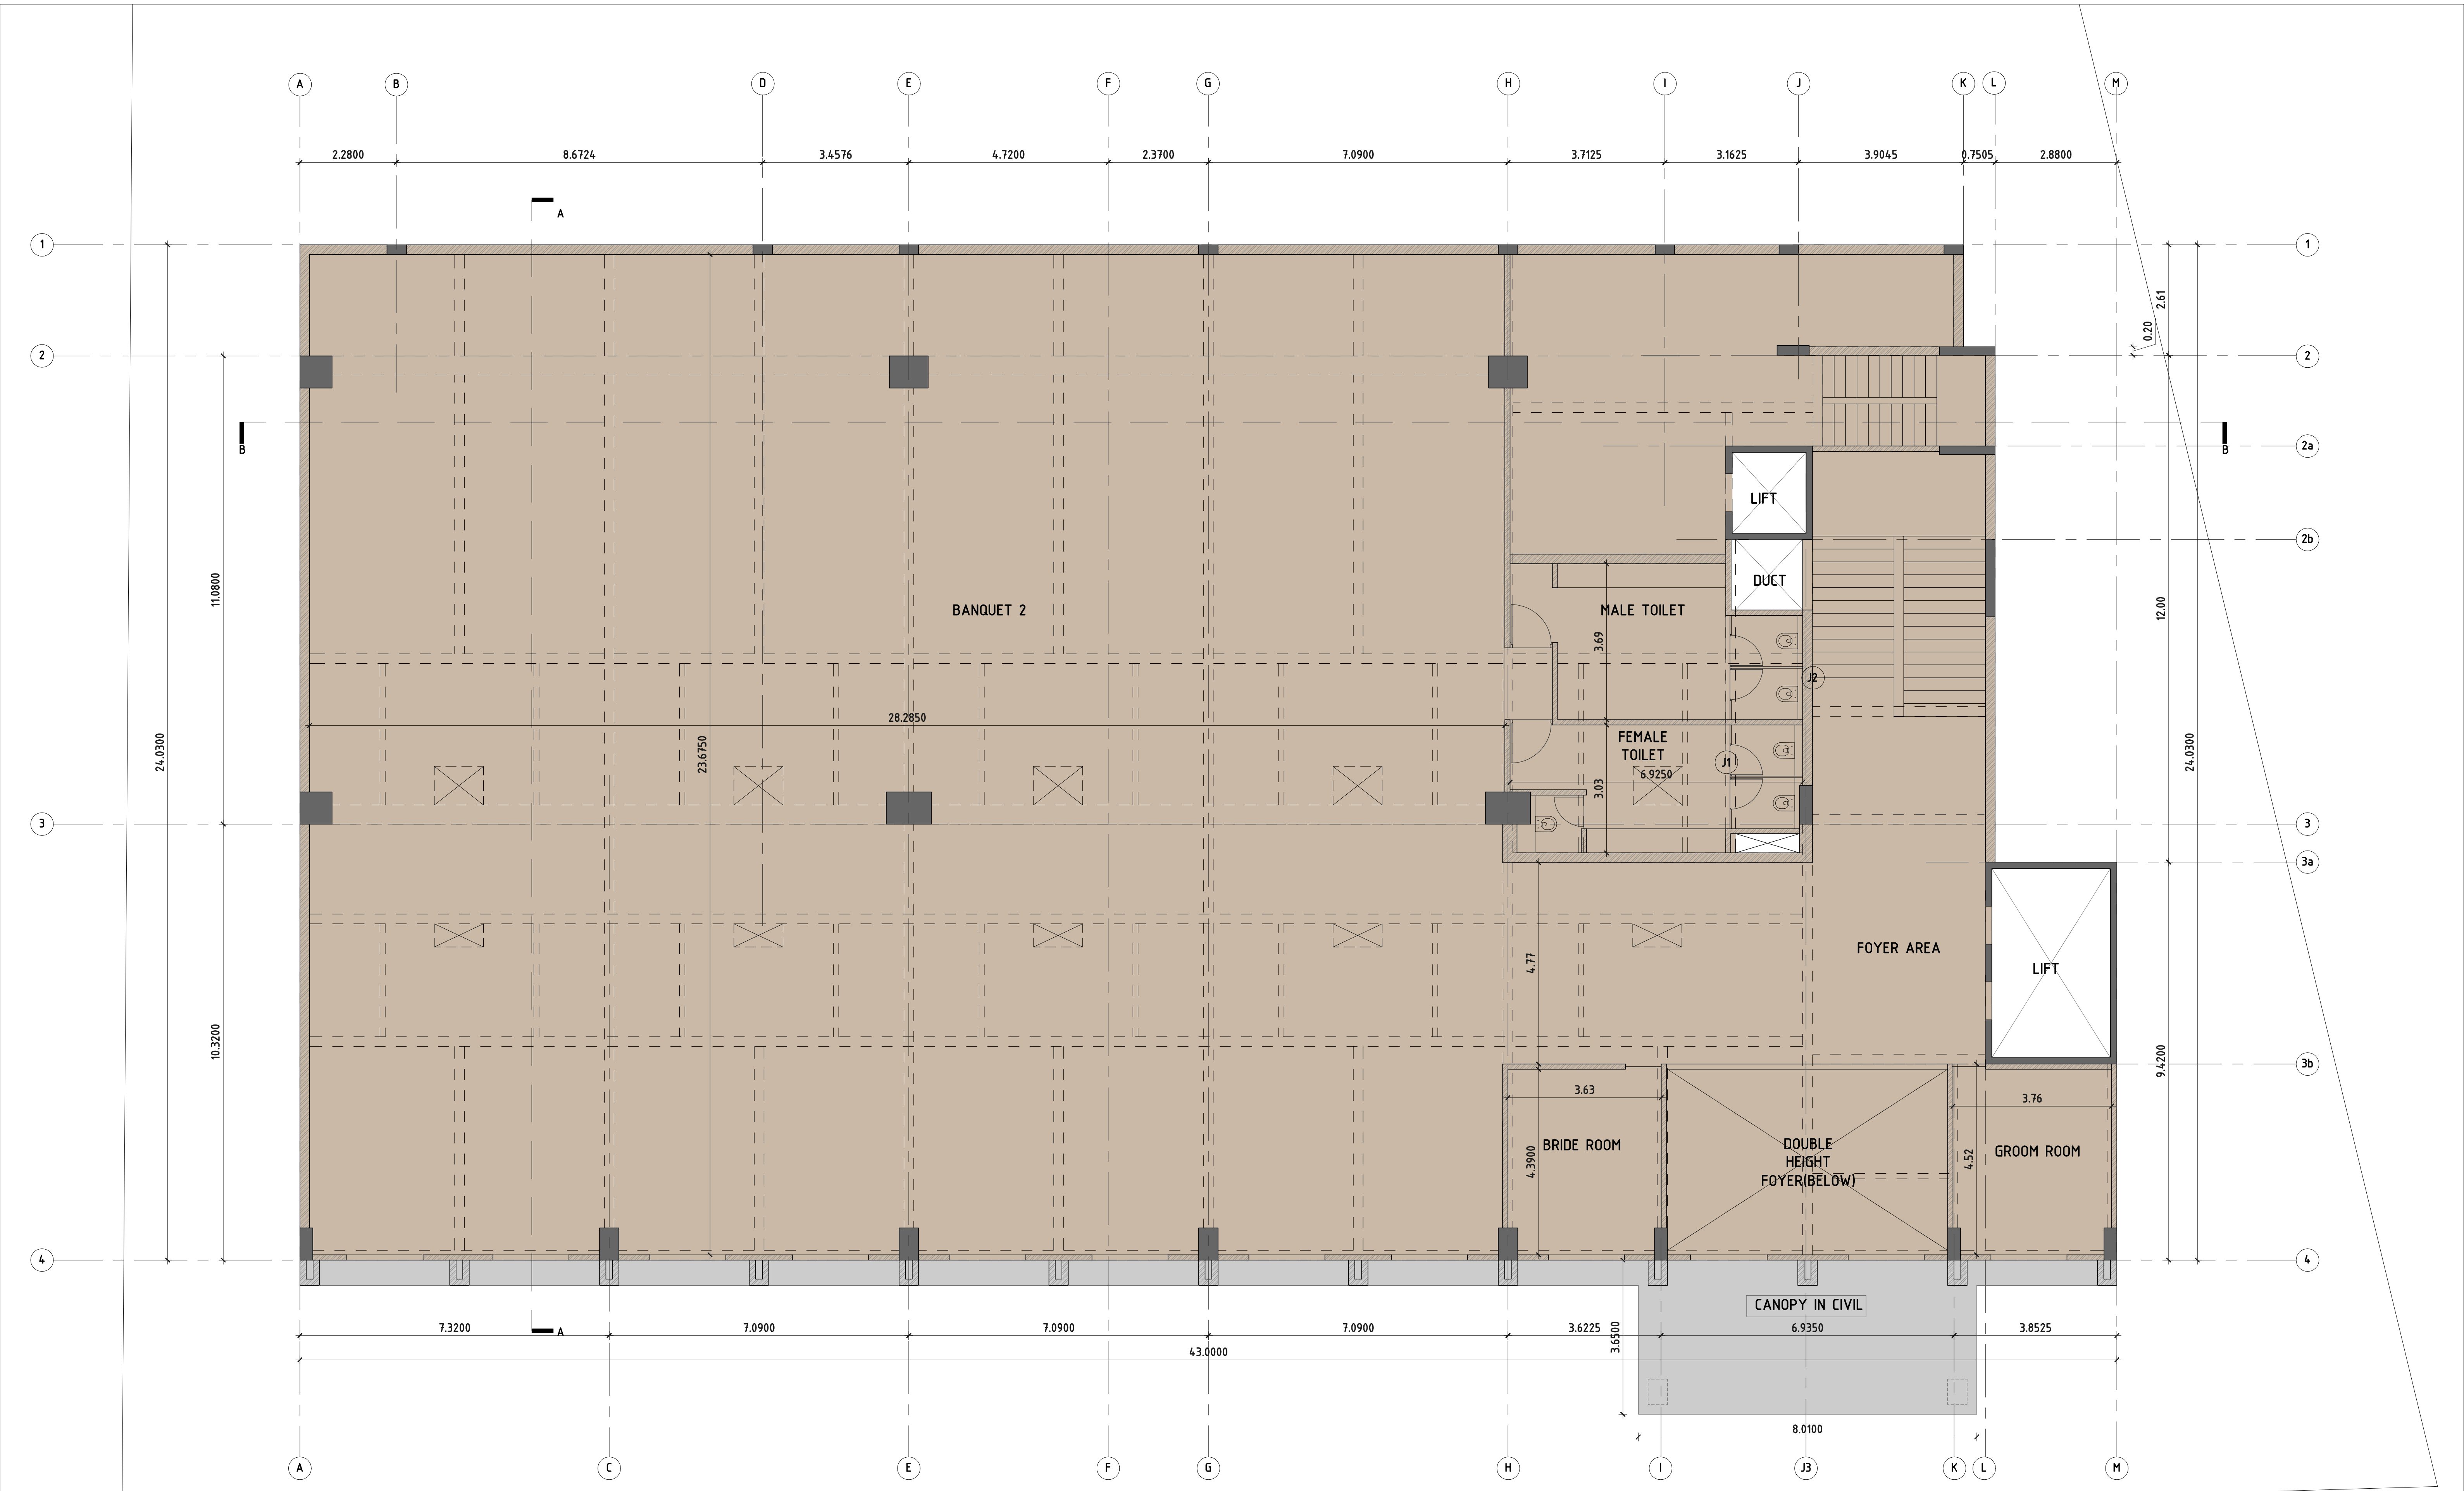

GENERAL NOTES :

- ALL DIMENSIONS ARE IN METRE
- ALL MEASUREMENTS ARE FROM UNFINISHED SURFACE TO UNFINISHED SURFACE. UNTILL OTHER SPECIFIED
- ALL DIMENSIONS ARE TO BE READ AND NOT TO BE MEASURED.
- DRIP MOULD IS TO BE PROVIDED AT ALL EXTERNAL WINDOW LINTELS
- CHICKEN MESH TO BE PROVIDED AT EVERY JUNCTION OF BRICK AND CONCRETE TO BE PLASTERED.
- IN CASE OF ANY AMBIGUITIES ON SITE, TH ARCHITECT SHOULD BE INFORMED.
- IT IS MUST TO INFORM AND TO HAVE PRIOR PERMISSION OF ARCHITECT BEFORE MAKING ANY CHANGES ON SITE.
- REFER THE LATEST REVISED DRAWING.
- IT IS MUST FOR RESPECTIVE SITE ENGINEER TO CHECK & CO-RELATE STRUCTURAL DRAWINGS WITH ARCHITECTURAL DRAWINGS

- ALL RCC WORKS, FOUNDATION & U.G.W.T DETAILS TO BE APPROVED FROM STRUCTURAL ENGINEER.
- ALL DRAWINGS SHALL BE READ IN CONJUNCTION WITH ALL OTHER RELEVANT DRAWINGS, TOGETHER WITH THE SPECIFICATIONS.
- IN CASE OF ANY DISCREPANCY BETWEEN ARCHITECTURAL DRGS. AND OTHER DRGS, DISCREPANCY SHOULD BE BROUGHT TO THE NOTICE OF THE ARCHITECT BEFORE COMMENCEMENT OF THE WORK.

DRAWING DETAIL

FIRST LAYOUT PLAN

ONLY FOR REFERENCE

DWG NO	DATE	NORTH
PL-203	R0 05 DEC 2025	
	R1	
	R2	
DWG BY	CHECKED	SCALE
NIRALEE	BIPINCHANDRA	N.T.S

CLIENT

ROYAL LANDMARK HOTEL

STRUCTURE : Modi consultant
- 91-9904752590

25001

PROJECT


ARCHITECT

ROYAL LANDMARK HOTEL

AT HIMMATNAGAR

AVASITI DESGIN CONSULTANCY PVT. LTD.

401,SHASTRA,
OPP.DRIVE IN CINEMA, DRIVE IN ROAD,
AHMEDABAD -380054,GUJARAT,INDIA
E : adc@avasiti.in , www.avasiti.in
PH: 079 40323308

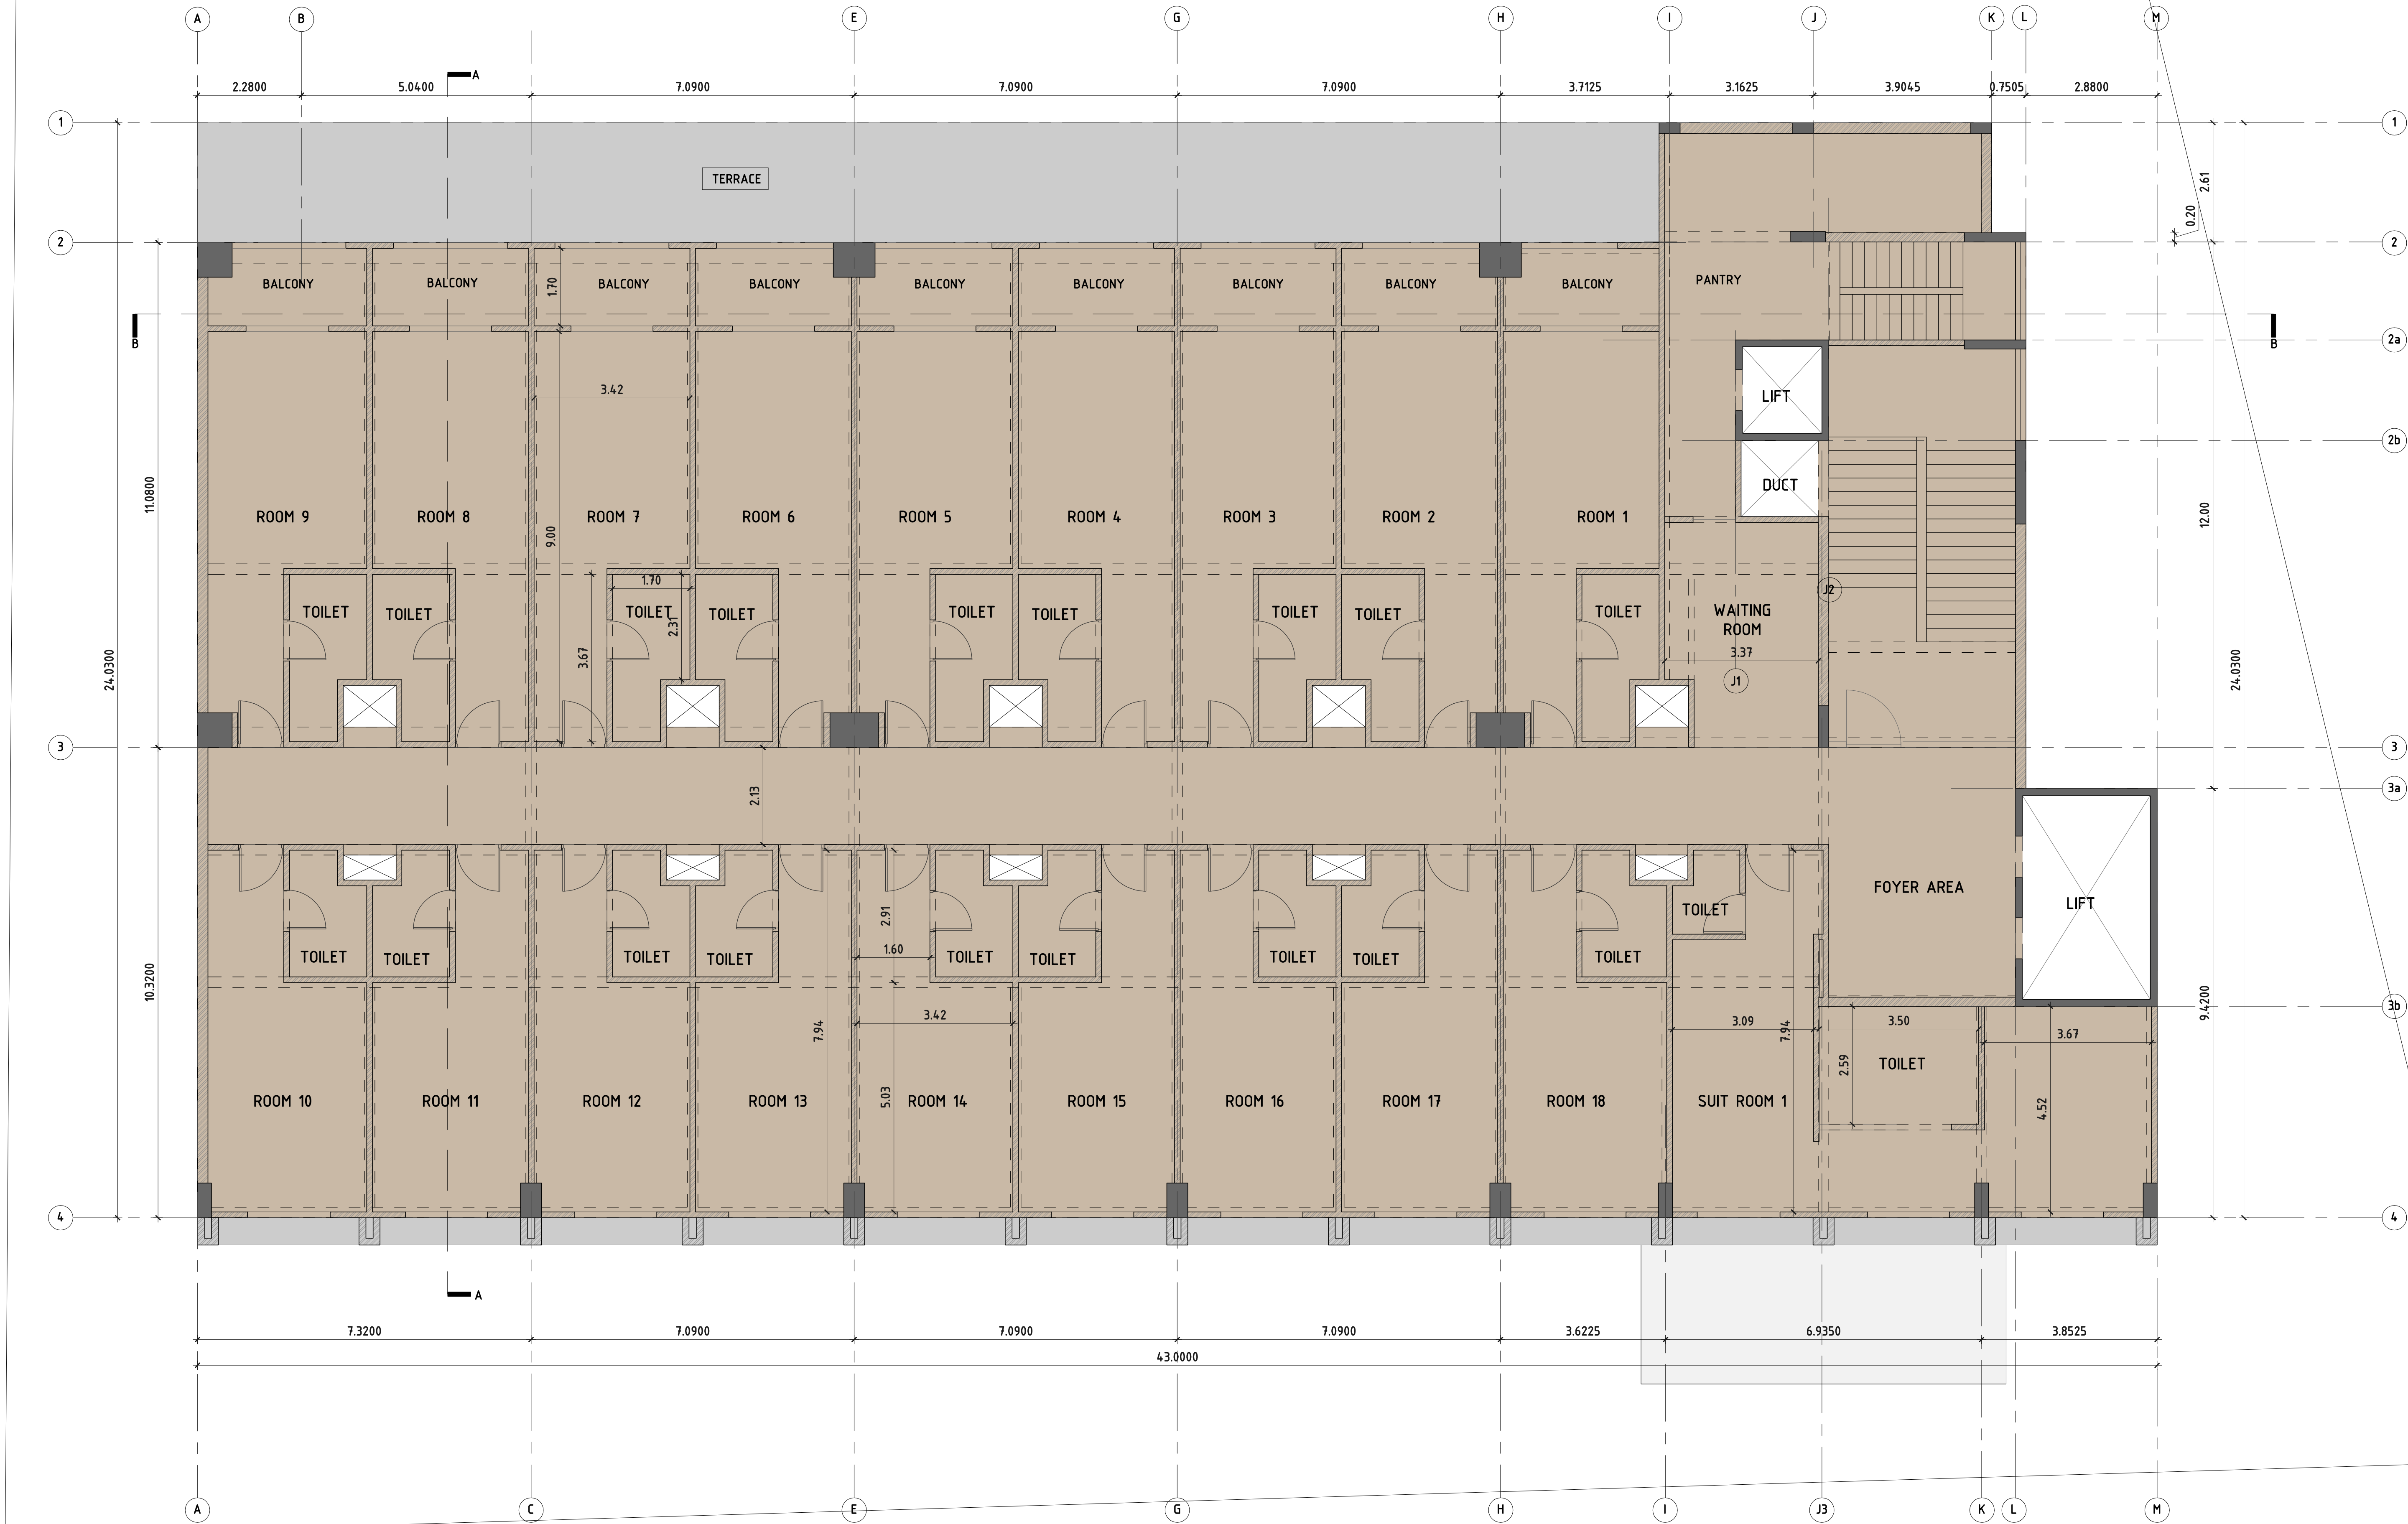

- GENERAL NOTES :
- ALL DIMENSIONS ARE IN METRE
 - ALL MEASUREMENTS ARE FROM UNFINISHED SURFACE TO UNFINISHED SURFACE. UNTILL OTHER SPECIFIED
 - ALL DIMENSIONS ARE TO BE READ AND NOT TO BE MEASURED.
 - DRIP MOULD IS TO BE PROVIDED AT ALL EXTERNAL WINDOW LINTELS
 - CHICKEN MESH TO BE PROVIDED AT EVERY JUNCTION OF BRICK AND CONCRETE TO BE PLASTERED.
 - IN CASE OF ANY AMBIGUITIES ON SITE, TH ARCHITECT SHOULD BE INFORMED.
 - IT IS MUST TO INFORM AND TO HAVE PRIOR PERMISSION OF ARCHITECT BEFORE MAKING ANY CHANGES ON SITE.
 - REFER THE LATEST REVISED DRAWING.
 - IT IS MUST FOR RESPECTIVE SITE ENGINEER TO CHECK & CO-RELATE STRUCTURAL DRAWINGS WITH ARCHITECTURAL DRAWINGS

- ALL RCC WORKS, FOUNDATION & U.G.W.T DETAILS TO BE APPROVED FROM STRUCTURAL ENGINEER.
- ALL DRAWINGS SHALL BE READ IN CONJUNCTION WITH ALL OTHER RELEVANT DRAWINGS, TOGETHER WITH THE SPECIFICATIONS.
- IN CASE OF ANY DISCREPANCY BETWEEN ARCHITECTURAL DRGS. AND OTHER DRGS, DISCREPANCY SHOULD BE BROUGHT TO THE NOTICE OF THE ARCHITECT BEFORE COMMENCEMENT OF THE WORK.

DRAWING DETAIL		
SECOND LAYOUT PLAN		
ONLY FOR REFERENCE		
DWG NO	DATE	NORTH
PL-204	R0 05 DEC 2025	
	R1	
	R2	
DWG BY	CHECKED	SCALE
NIRALEE	BIPINCHANDRA	N.T.S


CLIENT	ROYAL LANDMARK HOTEL
CONSULTANTS	STRUCTURE : Modi consultant - 91-9904752590

PROJECT	ROYAL LANDMARK HOTEL AT HIMMATNAGAR
ARCHITECT	 AVASITI DESGIN CONSULTANCY PVT. LTD. 401,SHASTRA, OPP.DRIVE IN CINEMA, DRIVE IN ROAD, AHMEDABAD -380054,GUJARAT,INDIA E : adc@avasiti.in , www.avasiti.in PH: 079 40323308



- GENERAL NOTES :
- ALL DIMENSIONS ARE IN METRE
 - ALL MEASUREMENTS ARE FROM UNFINISHED SURFACE TO UNFINISHED SURFACE. UNTILL OTHER SPECIFIED
 - ALL DIMENSIONS ARE TO BE READ AND NOT TO BE MEASURED.
 - DRIP MOULD IS TO BE PROVIDED AT ALL EXTERNAL WINDOW LINTELS
 - CHICKEN MESH TO BE PROVIDED AT EVERY JUNCTION OF BRICK AND CONCRETE TO BE PLASTERED.
 - IN CASE OF ANY AMBIGUITIES ON SITE, TH ARCHITECT SHOULD BE INFORMED.
 - IT IS MUST TO INFORM AND TO HAVE PRIOR PERMISSION OF ARCHITECT BEFORE MAKING ANY CHANGES ON SITE.
 - REFER THE LATEST REVISED DRAWING.
 - IT IS MUST FOR RESPECTIVE SITE ENGINEER TO CHECK & CO-RELATE STRUCTURAL DRAWINGS WITH ARCHITECTURAL DRAWINGS


- ALL RCC WORKS, FOUNDATION & U.G.W.T DETAILS TO BE APPROVED FROM STRUCTURAL ENGINEER.
- ALL DRAWINGS SHALL BE READ IN CONJUNCTION WITH ALL OTHER RELEVANT DRAWINGS, TOGETHER WITH THE SPECIFICATIONS.
- IN CASE OF ANY DISCREPANCY BETWEEN ARCHITECTURAL DRGS. AND OTHER DRGS, DISCREPANCY SHOULD BE BROUGHT TO THE NOTICE OF THE ARCHITECT BEFORE COMMENCEMENT OF THE WORK.

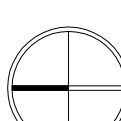DRAWING DETAIL				CLIENT
THIRD LAYOUT PLAN ONLY FOR REFERENCE				
DWG NO	DATE		NORTH	CONSULTANTS
PL-205	R0	05 DEC 2025		
	R1			
	R2			
DWG BY	CHECKED		SCALE	
NIRALEE	BIPINCHANDRA		N.T.S	

CLIENT	ROYAL LANDMARK HOTEL
	STRUCTURE : Modi consultant - 91-9904752590

PROJECT	25001
	ROYAL LANDMARK HOTEL AT HIMMATNAGAR
ARCHITECT	
	AVASITI DESGIN CONSULTANCY PVT. LTD. 401,SHASTRA, OPP.DRIVE IN CINEMA, DRIVE IN ROAD, AHMEDABAD -380054,GUJARAT,INDIA E : adc@avasiti.in , www.avasiti.in PH: 079 40323308

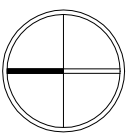

GENERAL NOTES :	● ALL DIMENSIONS ARE IN METRE ● ALL MEASUREMENTS ARE FROM UNFINISHED SURFACE TO UNFINISHED SURFACE. UNTILL OTHER SPECIFIED ● ALL DIMENSIONS ARE TO BE READ AND NOT TO BE MEASURED. ● DRIP MOULD IS TO BE PROVIDED AT ALL EXTERNAL WINDOW LINTELS ● CHICKEN MESH TO BE PROVIDED AT EVERY JUNCTION OF BRICK AND CONCRETE TO BE PLASTERED. ● IN CASE OF ANY AMBIGUITIES ON SITE, TH ARCHITECT SHOULD BE INFORMED. ● IT IS MUST TO INFORM AND TO HAVE PRIOR PERMISSION OF ARCHITECT BEFORE MAKING ANY CHANGES ON SITE. ● REFER THE LATEST REVISED DRAWING. ● IT IS MUST FOR RESPECTIVE SITE ENGINEER TO CHECK & CO-RELATE STRUCTURAL DRAWINGS WITH ARCHITECTURAL DRAWINGS	● ALL RCC WORKS, FOUNDATION & U.G.W.T DETAILS TO BE APPROVED FROM STRUCTURAL ENGINEER. ● ALL DRAWINGS SHALL BE READ IN CONJUNCTION WITH ALL OTHER RELEVANT DRAWINGS, TOGETHER WITH THE SPECIFICATIONS. ● IN CASE OF ANY DISCREPANCY BETWEEN ARCHITECTURAL DRGS. AND OTHER DRGS, DISCREPANCY SHOULD BE BROUGHT TO THE NOTICE OF THE ARCHITECT BEFORE COMMENCEMENT OF THE WORK.	DRAWING DETAIL			CLIENT CONSULTANTS	ROYAL LANDMARK HOTEL	25001	PROJECT	ROYAL LANDMARK HOTEL AT HIMMATNAGAR
			SECTION AA ONLY FOR REFERENCE				STRUCTURE : Modi consultant - 91-9904752590		ARCHITECT	अवसिति AVASITI DESGIN CONSULTANCY PVT. LTD. 401,SHASTRA, OPP.DRIVE IN CINEMA, DRIVE IN ROAD, AHMEDABAD -380054,GUJARAT,INDIA E : adc@avasiti.in , www.avasiti.in PH: 079 40323308
			DWG NO	DATE			NORTH			
			PL-206	R0	05 DEC 2025					
				R1						
				R2						
			DWG BY	CHECKED	SCALE					
			NIRALEE	BIPINCHANDRA	N.T.S					



- GENERAL NOTES :
- ALL DIMENSIONS ARE IN METRE
 - ALL MEASUREMENTS ARE FROM UNFINISHED SURFACE TO UNFINISHED SURFACE. UNTILL OTHER SPECIFIED
 - ALL DIMENSIONS ARE TO BE READ AND NOT TO BE MEASURED.
 - DRIP MOULD IS TO BE PROVIDED AT ALL EXTERNAL WINDOW LINTELS
 - CHICKEN MESH TO BE PROVIDED AT EVERY JUNCTION OF BRICK AND CONCRETE TO BE PLASTERED.
 - IN CASE OF ANY AMBIGUITIES ON SITE, TH ARCHITECT SHOULD BE INFORMED.
 - IT IS MUST TO INFORM AND TO HAVE PRIOR PERMISSION OF ARCHITECT BEFORE MAKING ANY CHANGES ON SITE.
 - REFER THE LATEST REVISED DRAWING.
 - IT IS MUST FOR RESPECTIVE SITE ENGINEER TO CHECK & CO-RELATE STRUCTURAL DRAWINGS WITH ARCHITECTURAL DRAWINGS

- ALL RCC WORKS, FOUNDATION & U.G.W.T DETAILS TO BE APPROVED FROM STRUCTURAL ENGINEER.
- ALL DRAWINGS SHALL BE READ IN CONJUNCTION WITH ALL OTHER RELEVANT DRAWINGS, TOGETHER WITH THE SPECIFICATIONS.
- IN CASE OF ANY DISCREPANCY BETWEEN ARCHITECTURAL DRGS. AND OTHER DRGS, DISCREPANCY SHOULD BE BROUGHT TO THE NOTICE OF THE ARCHITECT BEFORE COMMENCEMENT OF THE WORK.

SECTION BB		
ONLY FOR REFERENCE		
DWG NO	DATE	NORTH
PL-207	R0 05 DEC 2025	
	R1	
	R2	
DWG BY	CHECKED	SCALE
NIRALEE	BIPINCHANDRA	N.T.S

CLIENT	ROYAL LANDMARK HOTEL
CONSULTANTS	STRUCTURE : Modi consultant - 91-9904752590

PROJECT	ROYAL LANDMARK HOTEL AT HIMMATNAGAR
ARCHITECT	 AVASITI DESGIN CONSULTANCY PVT. LTD. 401,SHASTRA, OPP.DRIVE IN CINEMA, DRIVE IN ROAD, AHMEDABAD -380054,GUJARAT,INDIA E : adc@avasiti.in , www.avasiti.in PH: 079 40323308